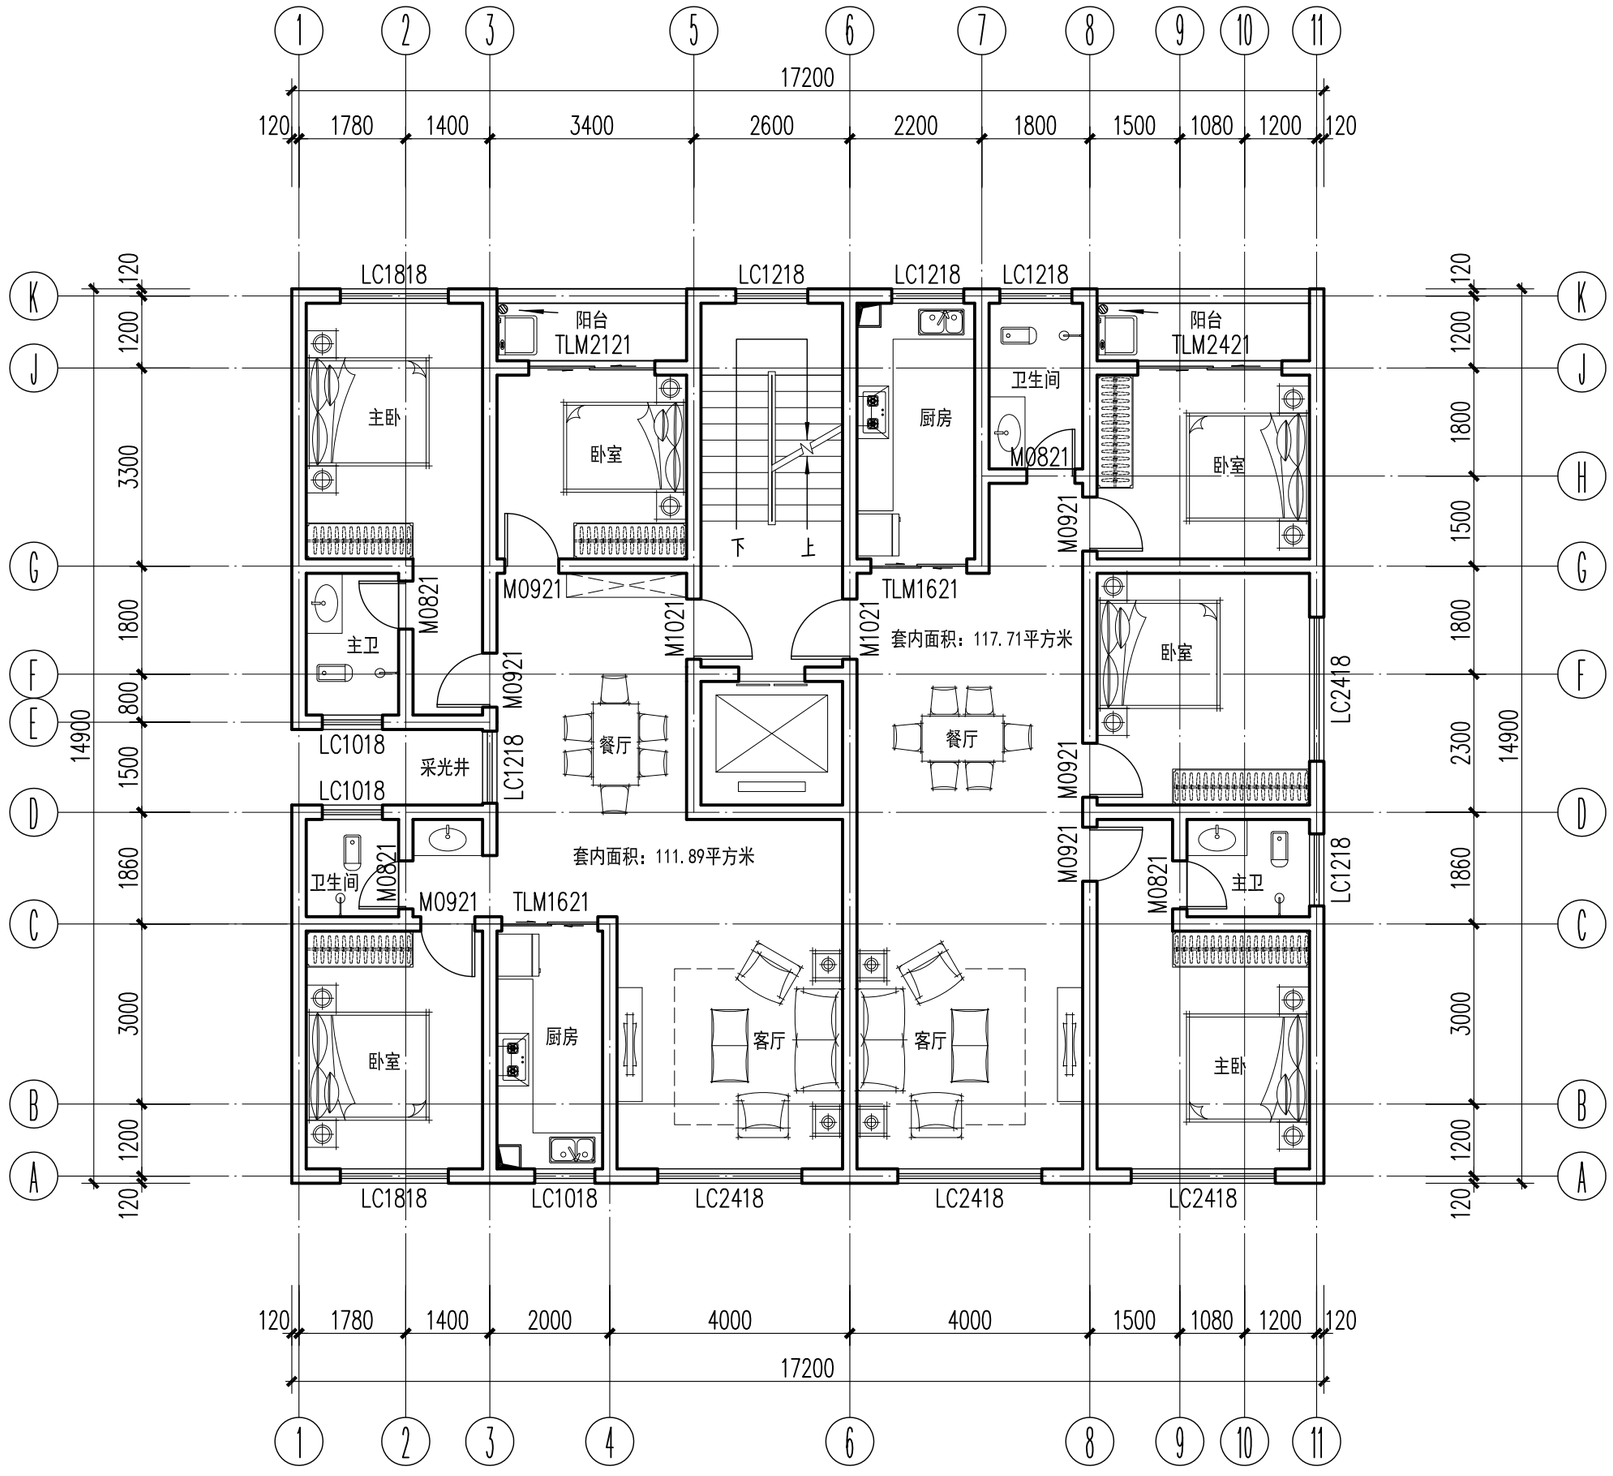


图例			
	挂式室内机		蹲便器
	空调室外机		淋浴
	厨房排烟道		洗手盆
	冰箱		洗菜盆
	洗衣机		燃气灶
R	燃气热水器		地漏
	空调冷凝管		卫生间预留洞

楼层标高表

楼层	标高(H)	楼层	标高(H)
首层	±0.000	五层	14.100
二层	4.500	六层	17.300
三层	7.700	架空隔热层	20.500
四层	10.900	屋面层	21.500

二至六层平面图 1:100

本层建筑面积：256.28平方米

湖南夫夷建筑勘察设计有限公司				建设单位	邵阳县塘渡口镇人民政府	
设计资质证书：A243008279				项目名称	邵阳县红石谢家居民安置区3栋51#谢小亮等	
项目负责人		注册师		二至六层平面图	设计号	
审核		校对			阶段	方案
审定		设计			图别图号	
					日期	2023.10